

SELECTED PROJECT

M A R I A C O R T E S

architecture

P R O J E C T P O R T F O L I O D E S I G N E R

ÍNDICE

+	<u>SOBRE MÍ</u>	01
+	<u>PROYECTO TESIS GRADO</u>	02
+	<u>PROYECTOS MASTER</u>	03
+	<u>PROYECTOS PROFESIONALES</u>	04

SOBRE MÍ

..... MARÍA CORTÉS VARGAS



HOLA! 🖐️

Soy Arquitecta con una sólida formación en arquitectura y diseño de espacios con más de 7 años de experiencia como arquitecta. Como diseñadora, tengo una pasión innata por traducir la complejidad en soluciones de diseño creativas, simples y funcionales.

Mi trabajo se destaca por la comunicación, eficacia y capacidad para resolver desafíos. Mantengo un enfoque proactivo y autodidacta en mi día a día, para estar siempre al día con las últimas tendencias y tecnologías, tengo experiencia tanto en coordinación como en trabajo en equipo, demostrando habilidades de adaptabilidad y organización.

IDIOMAS

Español / Spanish (Nativo)

Ingles / English (TOEFL)

Catalán / Català (A2)

CONTACTO



+34 663 58 50 81



mariacv1993@gmail.com



<https://www.linkedin.com/in/mariacortesv24/>



Barcelona, España

EXPERIENCIA

ARQUITECTA - Roarquitectos
Levantamiento y diseño de planos para proyectos de interiorismo, edificación y rehabilitaciones. Realización de mediciones y presupuestos, así como de certificados de eficiencia energética.

Feb. 2021 - Oct 2023 (2años y 9meses)
Barcelona, España

ARQUITECTA - Ministerio de Educación de la República Dominicana
Levantamiento y diseño de planos para Escuelas Públicas del País. Realización de mediciones y propuestas de construccion o rehabilitacion, así como de informes de mejoras.

Ene. 2017 - Dic. 2020 (4años)
Santo Domingo, RD

ARQUITECTA JUNIOR - Empresas Llobregat (Practicas)
Levantamiento y diseño de planos para proyectos de interiorismo, edificación y rehabilitaciones. Realización de mediciones y presupuestos. Diseño Grafico, Manejo de Redes Sociales y Encargada de Ventas.

Jun. 2015 - Dic. 2016 (1año)
Santo Domingo, RD

FORMACIÓN

CURSO EXPERTO EN ARQUITECTURA 3D
Escuela Superior GADE

Mar. 2023 - Abr. 2024
Barcelona, España

MASTER DISEÑO DE ESPACIOS: USER EXPERIENCE
EINA, Centro Universitario de Diseño y Arte de Bacelona

Nov. 2020 - Sept. 2021
Barcelona, España

ARQUITECTURA
Pontificia Universidad Católica Madre y Maestra (PUCMM)

Nov. 2020 - Sept. 2021
Santo Domingo, RD

SOFTWARES

- Diseño Arquitectonico 2D y 3D**
 - REVIT Architecture
 - AUTOCAD
 - 3D Max
 - VectorWorks
 - TWINMOTION
- Diseño**
 - Adobe Photoshop
 - Adob e Illustrator
 - Adobe InDesign
- Otros**
 - PRESTO
 - Ce3X (básico)
 - Final Cut Video Editor
 - Microsoft Word, PPT, Excel

The background features an abstract geometric design. It includes three red rectangles: one at the top left, one on the right side, and one at the bottom left. Black lines are also present: a horizontal line extending from the top rectangle, a vertical line extending from the right rectangle, and a horizontal line extending from the bottom rectangle.

PROYECTO

TESIS FINAL DE GRADO

La Arquitectura Efímera como
Espacio de Representación

Proyecto: La Arquitectura Efímera como espacio de Representación

DISEÑO DE UN ESPACIO CINEMÁTICO EN LOCACIÓN
2016-2017

PROBLEMATICA

En Santo domingo los espacios efimeros de representación en ocasiones no logran complementar la percepción y la plástica del espacio.

Si no se logra la representación deseada, el mensaje no es vivido, ni asimilado y el espacio se convierte en un contenedor de objetos y no de experiencias.

OBJETIVO

Analizar las condiciones espaciales de la arquitectura efimera en relación a la percepción del usuario, para la creación de un espacio de representación.



MARCO TEÓRICO

EL ESPACIO ARQUITECTÓNICO

"La Arquitectura no "modela" el espacio... Por lo tanto, no se configura el espacio; sino lo espacial o extenso..." (Morales, 1984, Pág. 147).

PERCEPCIÓN


"El desafío de la arquitectura consiste en estimular tanto la percepción interior como la exterior... mientras, simultáneamente, se expresa el significado..." (Holl, 2011, Pág. 12).

ARQUITECTURA EFÍMERA

"Condiciones como ligereza, autoconstrucción, economía, rapidez y sencillez de montaje y desmontaje... requieren utilizar el aspecto más innovador y de investigación arquitectónica." (Blasco, 2012, Pág. 17)



CONCLUSIONES

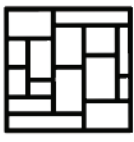

Flexibilidad



Adaptación



Relación



Percepción

VEHICULO

► DISEÑO DEL ESPACIO CINEMÁTICO EN LOCACIÓN REAL PARA UNA PELÍCULA.

Se diseñará un espacio arquitectónico efimero para una película. Basándonos en criterios de un diseño de producción, ya consensuado con el director del proyecto, se generarán estos espacios según lo establecido por el guion.

Se pretende fomentar una nueva oportunidad para arquitectos en el cine. Estos podrán experimentar y dar soluciones flexibles e innovadoras para los espacios cinemáticos, generando la representación necesaria para generar las sensaciones que se desean.

OPORTUNIDADES



Adaptación



Traslado



Flexibilidad



Costo Eficiente



Experimentación



Representación del concepto

RECOMENDACIONES



Escala



Luz



Plástica



Ensamblaje



Movimiento

Si se concibe el espacio efimero relacionando sus principios y los elementos perceptuales se logrará una representación conceptual favorable de cualquier espacio.

RELEVANCIA




PERTINENCIA



Profesional entrenado para diseñar y crear un espacio con los requerimientos necesarios para dejar un impacto en el espectador.

NECESIDAD

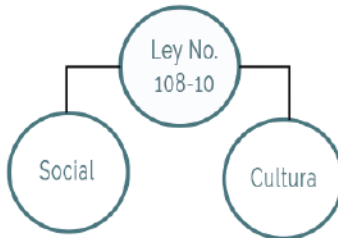

GRUPO HUMANO



Grupo Físico

En entrevista con Milbert Perez (Productor de la película) mencionó que para esta producción se estiman entre 50-70 personas trabajando en la misma. El crew de



GUIÓN / PELÍCULA



Collage película MATUM. Fuente: Dossier película MATUM, elaborado por Sullion Sang, con la instrucción e idea de Arq. Ico Abreu. (2014)

ESPACIOS / ESCENAS

A través de una cronología, se llegó a la conclusión de utilizar para la representación los espacios que más escenas tenían.

- HABITACIÓN 19



- EXPLANADA/FACHADA



- SALÓN DE FIESTAS



- BAR



- COCINA



- COMEDOR



- CORREDOR





- LOBBIES





PROPUESTA

Para la propuesta se analizó el espacio como era en su estado original en 1965 y en la actualizad 2017, por lo que se propueso la recreación de la fachada completa con un panel falso por encima de la original. Debido a la diferencia e tamaños se creará una estructura auto portante del lado oeste para completar la fachada construyendo tambien una plataforma debajo para nivelar. Todo el frente en su base sera cubierto de follaje para camuflar la estructura.



Se realiza ua comparacion de las plantas, para ver similitudes y diferencias. Con esto se puede decidir en que espacios se diseñarán los sets. Gracias a esto se propusieron las ubicaciones en diferentes espacios que cumplan con los metrajes requeridos.

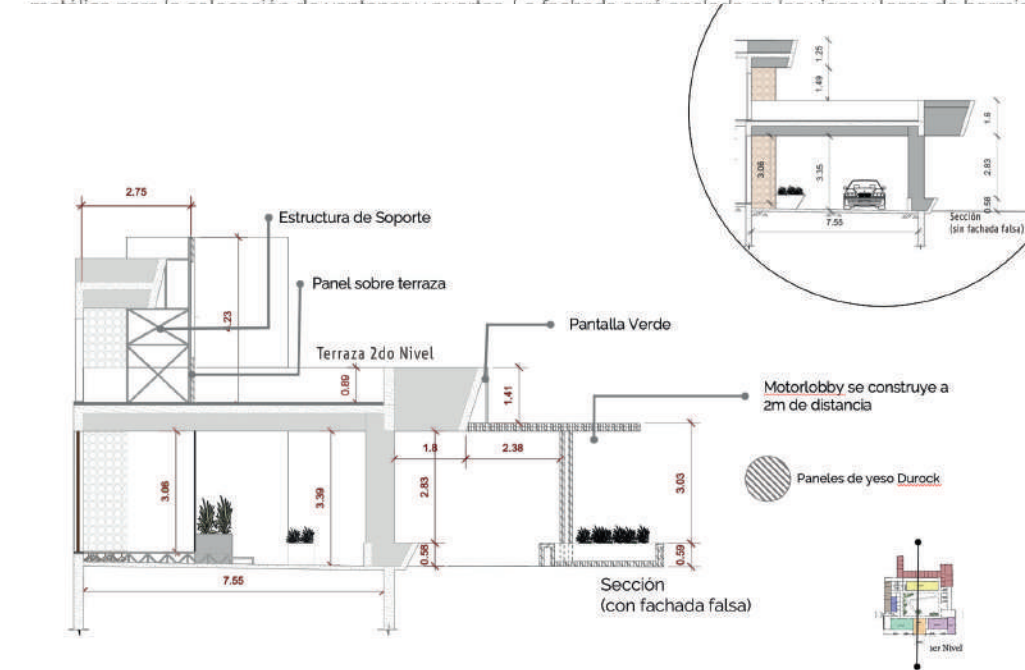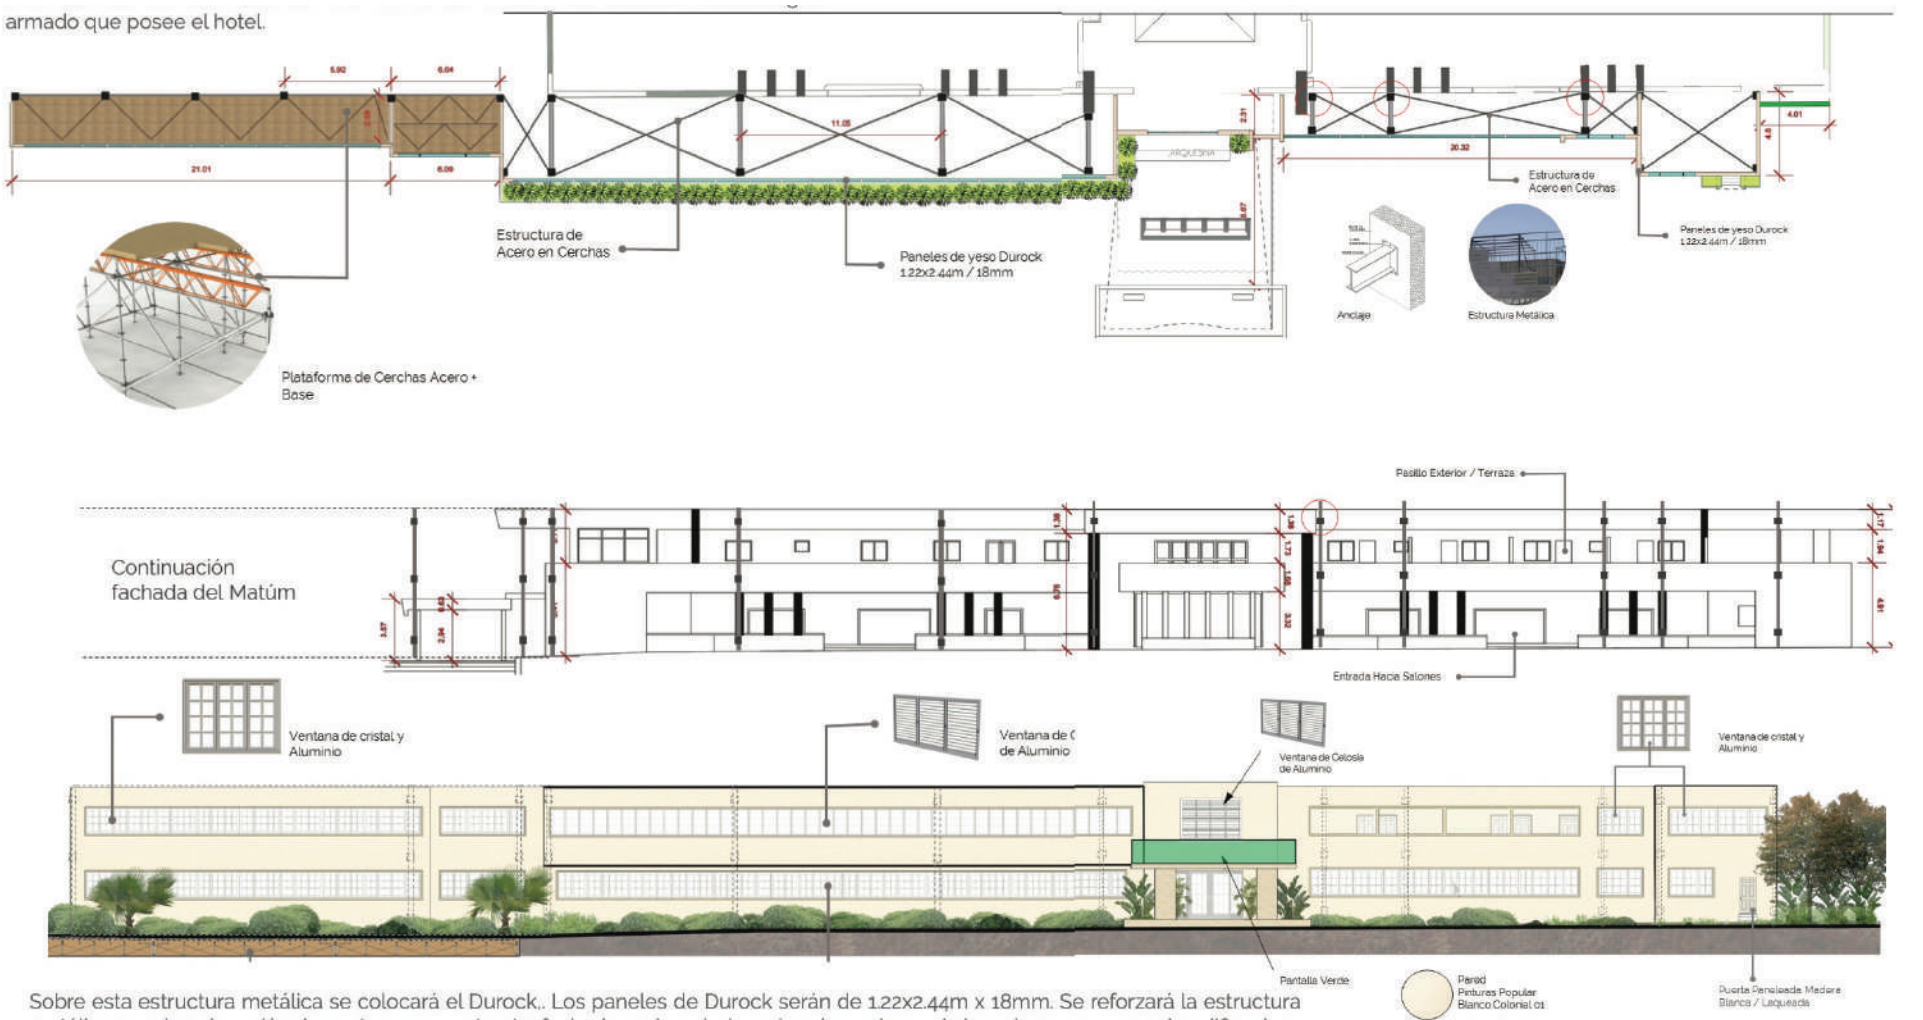


LOBBIES PLANTAS

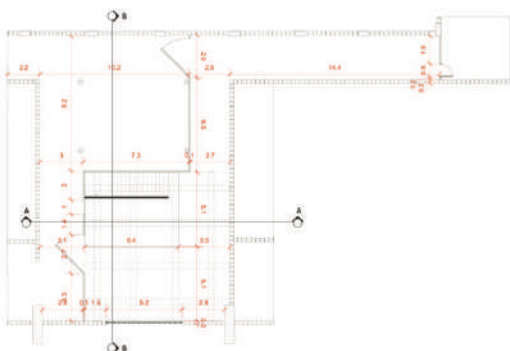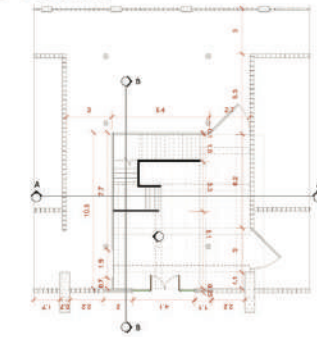


LOBBIES SECCION

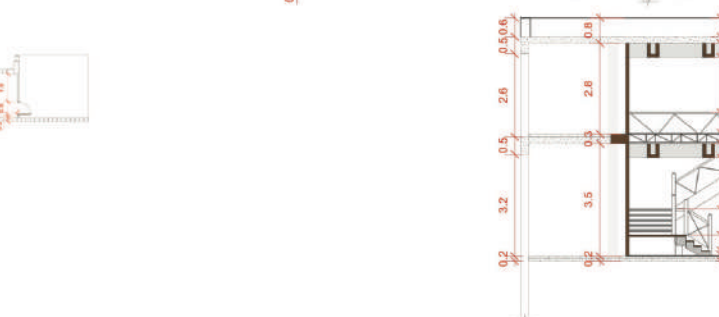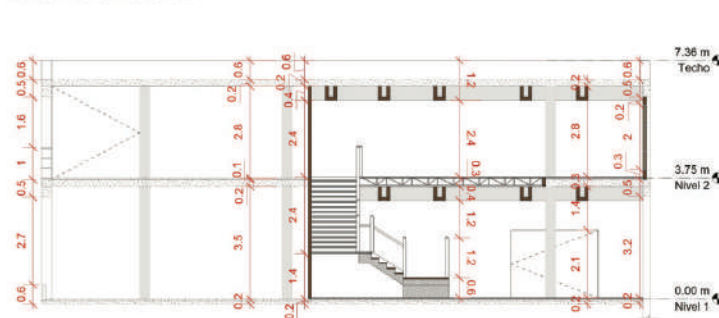

LOBBIES MATERIALIDAD

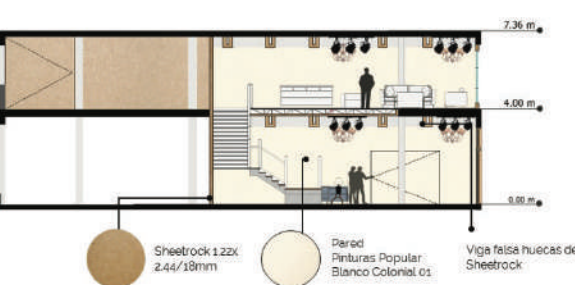

BAR SECCIONES

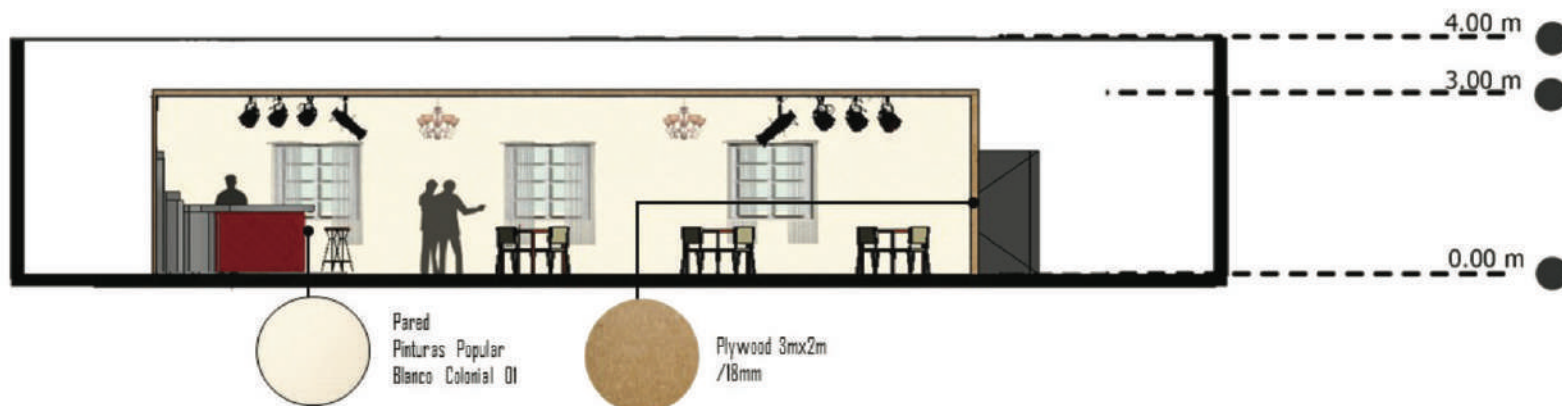

Piso Mármol
veteado
0.50x0.50m


Pared
Pinturas
Popular
Blanco Colonial
01




Paneles Móviles









Puerta doble batiente
Madera Blanca / Laqueada

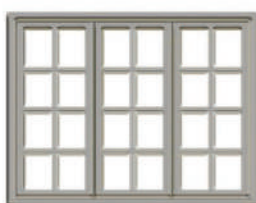

Ventana de Cristal
y Aluminio

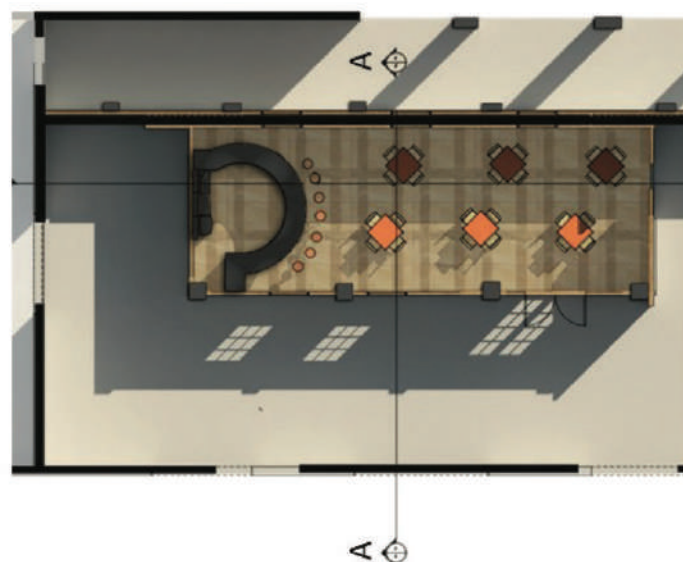[illegible][illegible]

HABITACIÓN

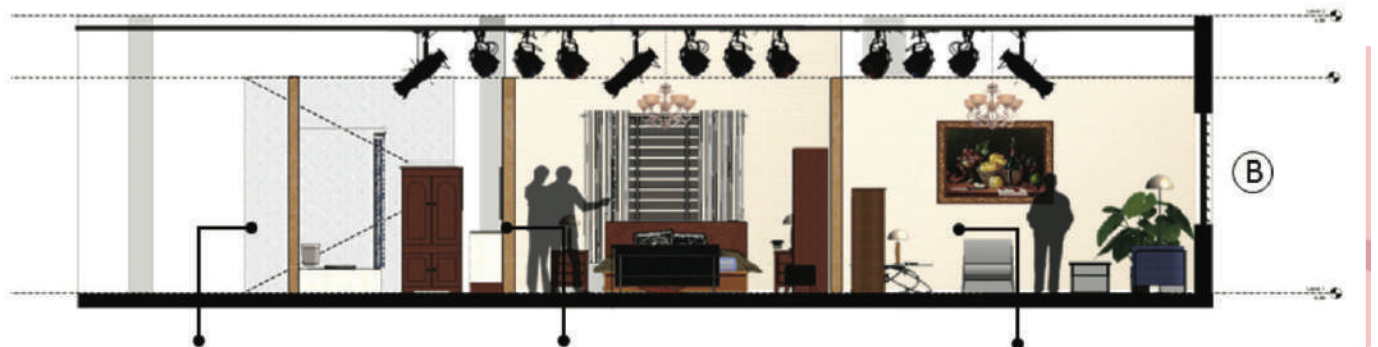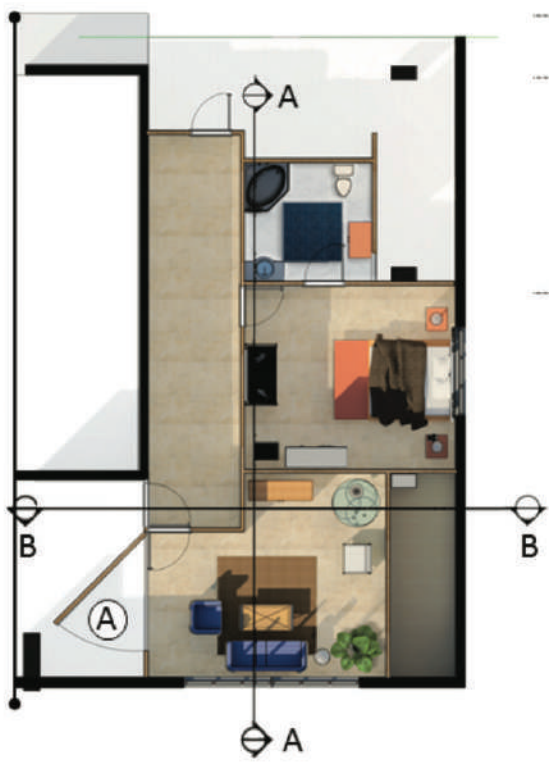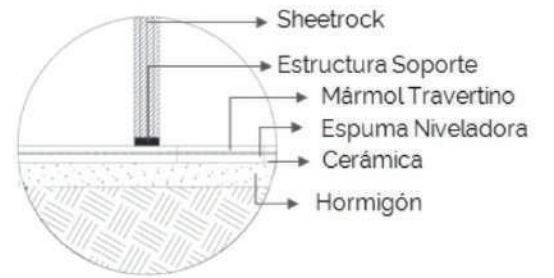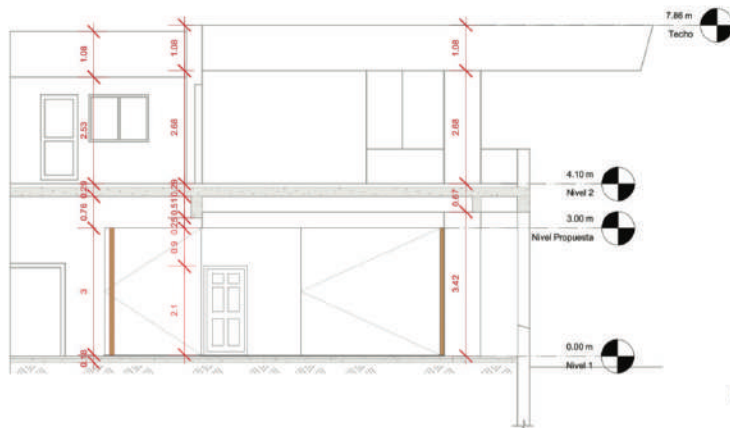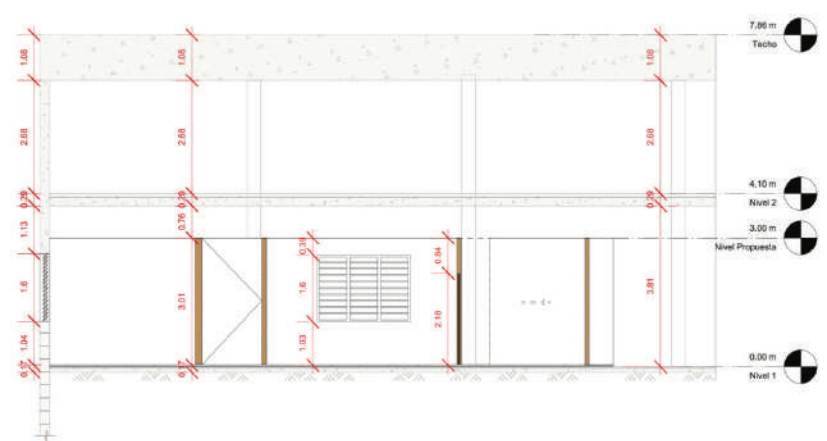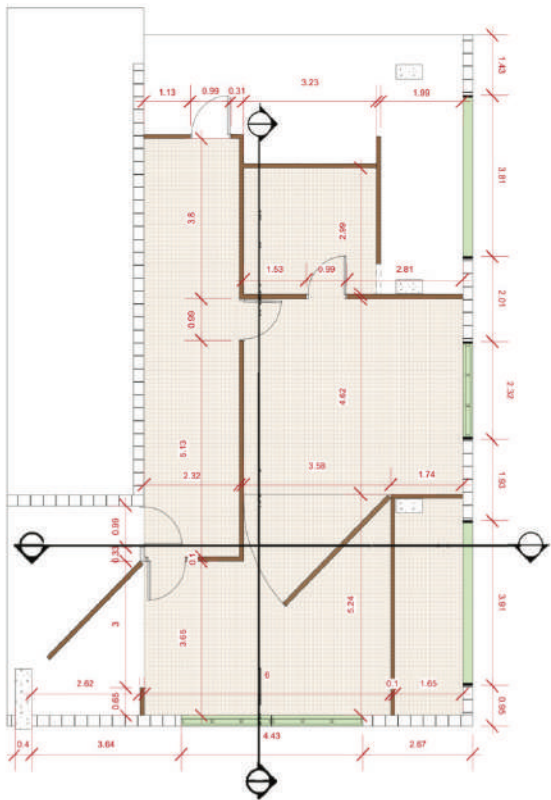

Para la construcción de las paredes de los sets se utilizará:




Paneles Móviles



Puerta Paneleada Madera Blanca / Laqueada





B Ventana de Celosía de Aluminio

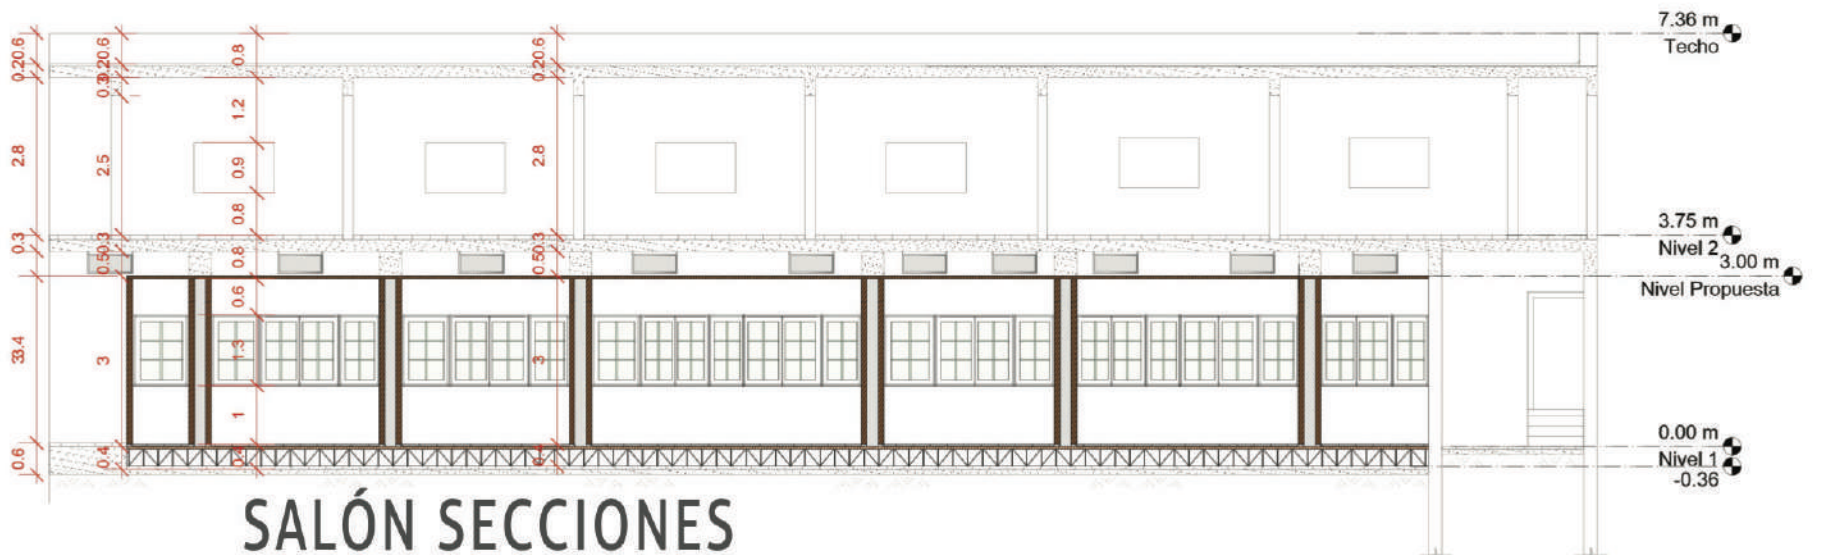


SALÓN SECCIONES

DETALLE I
 Esc.: 1:50

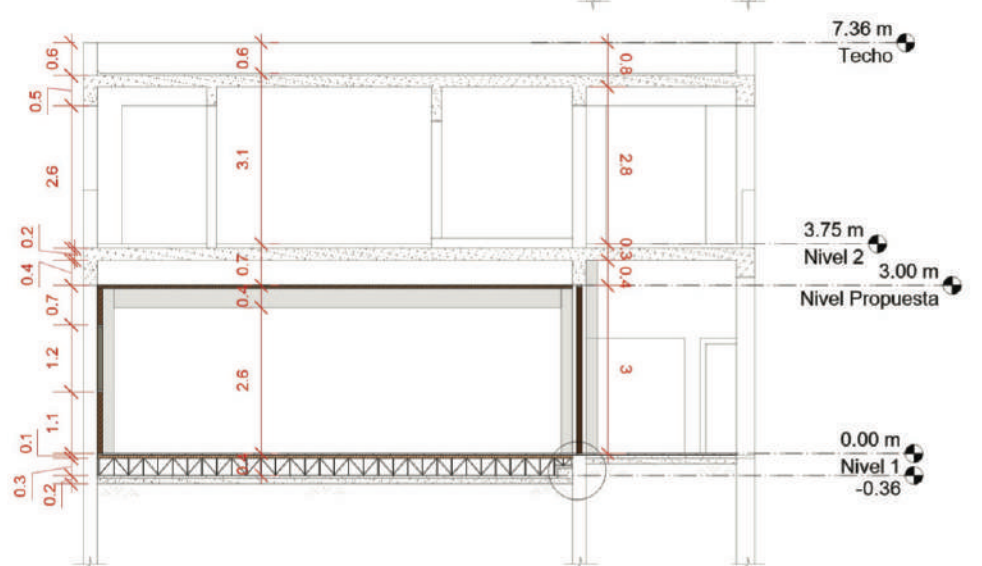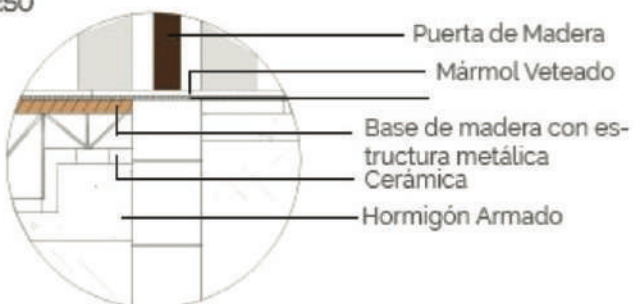

SALON

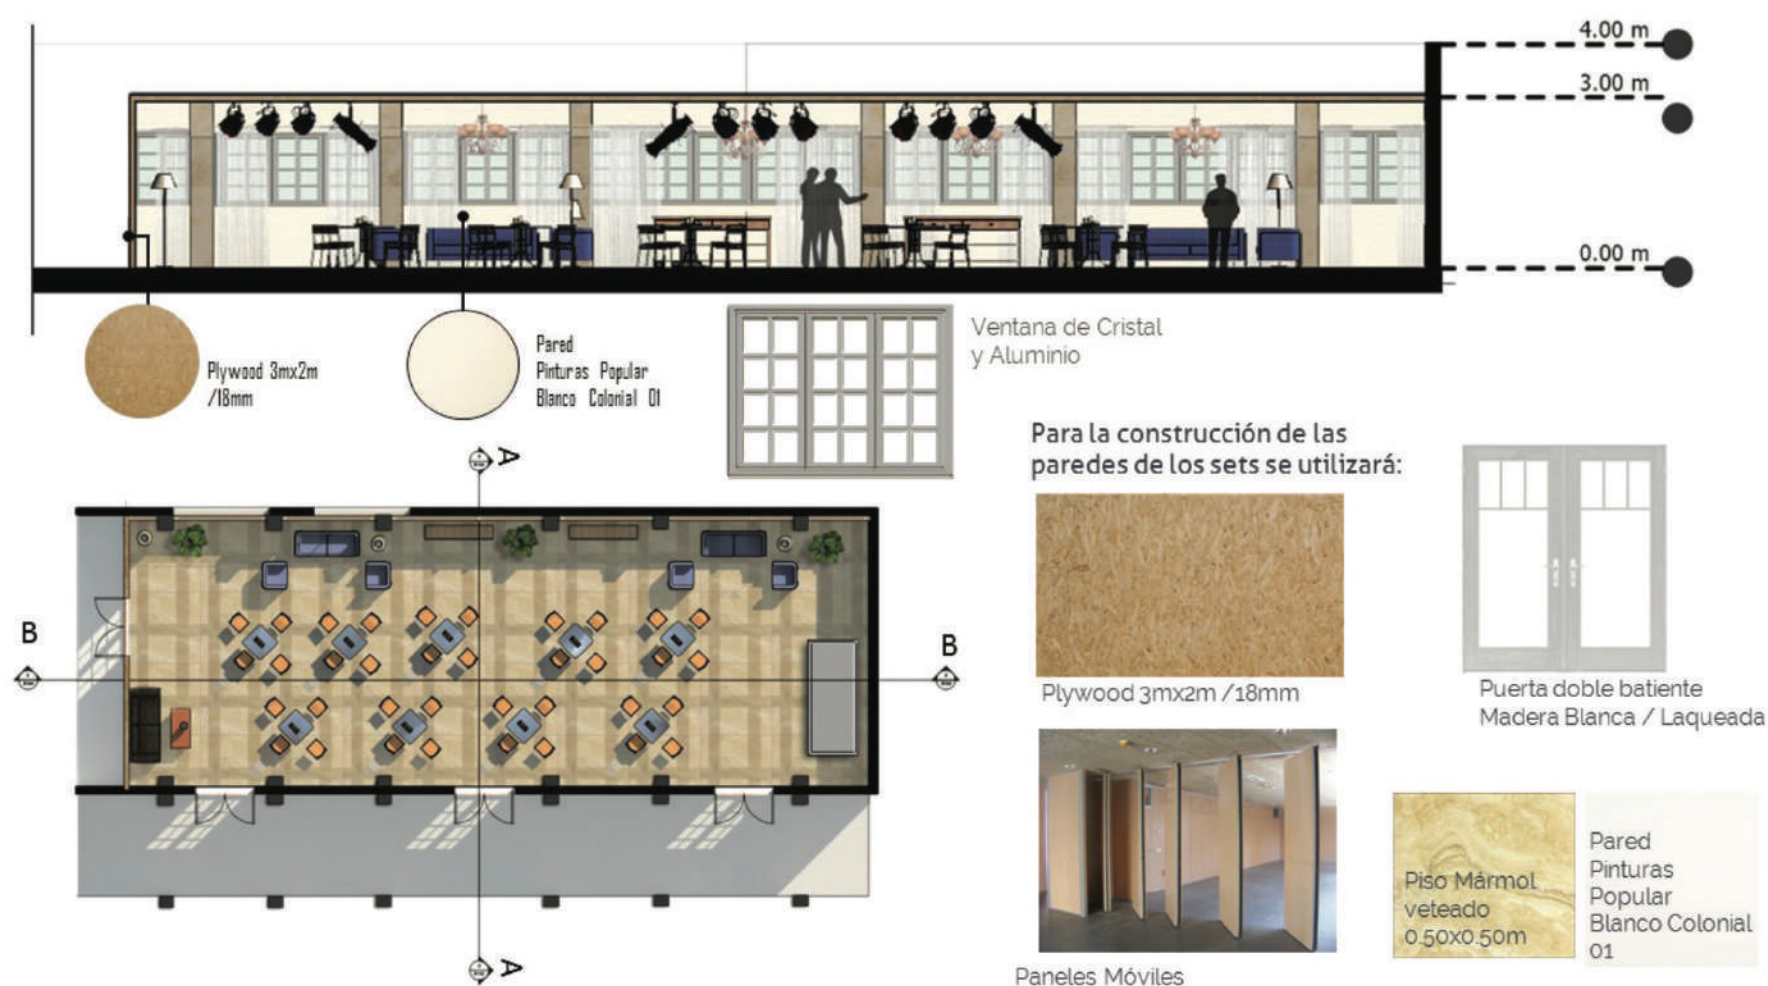

VISTAS 3D





P R O Y E C T O S

MASTER DISEÑO DE
ESPACIOS: USER
EXPERIENCE





RESIDENTIAL DESIGN



2021

Propuesta casa Kenna

Durante el curso de Diseño Residencial, llevamos a cabo un proyecto de rehabilitación de viviendas. En este proyecto, cada estudiante seleccionó un usuario para el cual diseñarían una propuesta de rehabilitación de su hogar. Personalmente, elegí trabajar en un proyecto destinado a Mckenna, conocida como Cozykitzune en las redes sociales. Mckenna es una influencer youtuber con un estilo peculiar que abarca elementos vintage, boho y toques de estilos victorianos/renacentistas modernos, a veces con influencias japonesas. Durante el proyecto, realicé un análisis detallado de sus hábitos y patrones de vida, considerando su estilo de vida como persona soltera que cocina poco y trabaja desde casa. El objetivo principal fue diseñar un espacio que reflejara su personalidad distintiva y que al mismo tiempo fuera cómodo y funcional para sus actividades diarias.



Planta y Sección Original

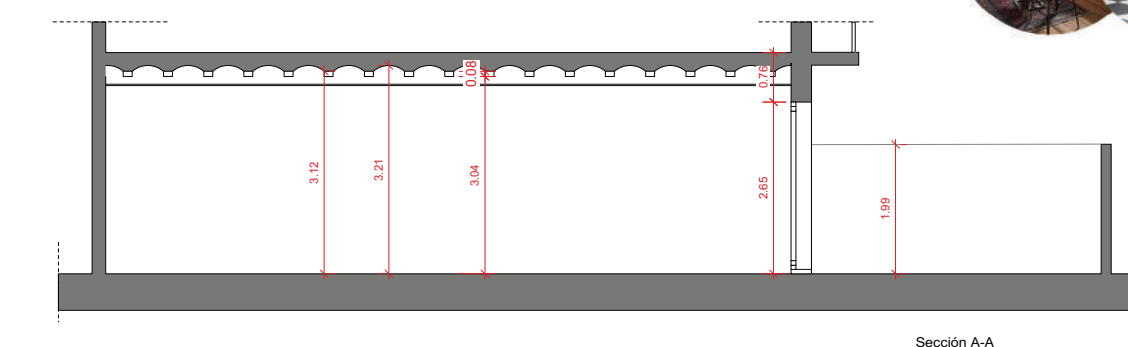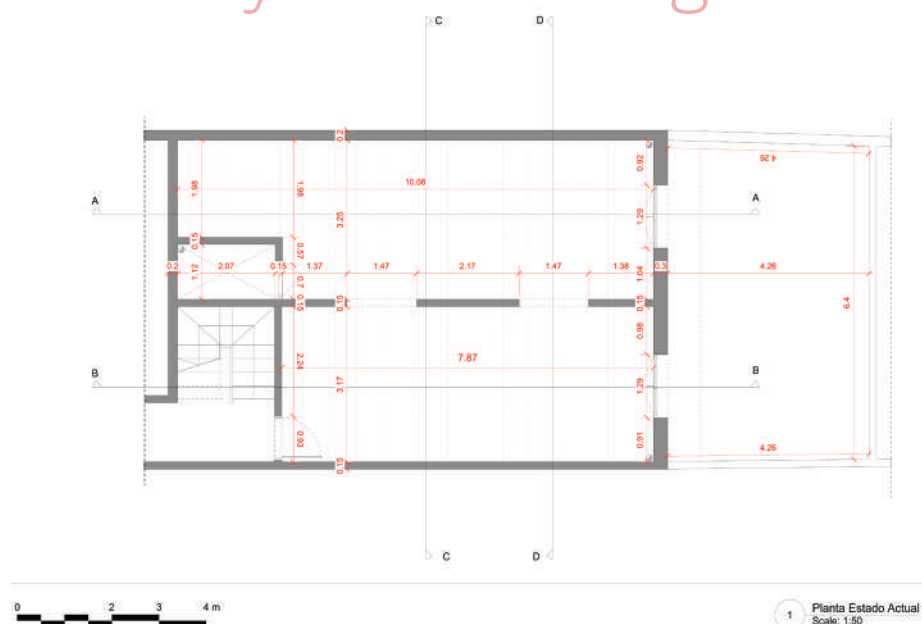


Sección A-A

Zonifiacion




Planos Propuesta Casa Kenna

Para la propuesta, me centré en el diseño de un espacio abierto que integra la cocina y el salón, priorizando especialmente el diseño de la cocina, considerando que no será utilizada con frecuencia. Me enfoqué en crear un ambiente de salón con un estilo vintage/boho, utilizando mobiliario reutilizable y elementos decorativos que reflejen su estética única. Además, dediqué atención al diseño del dormitorio/oficina, incorporando un amplio espacio de almacenamiento para acomodar sus pertenencias, dadas sus actividades como influencer y trabajos manuales. Se diseñó una terraza para proporcionar un espacio adicional donde pueda relajarse y grabar contenido al aire libre.

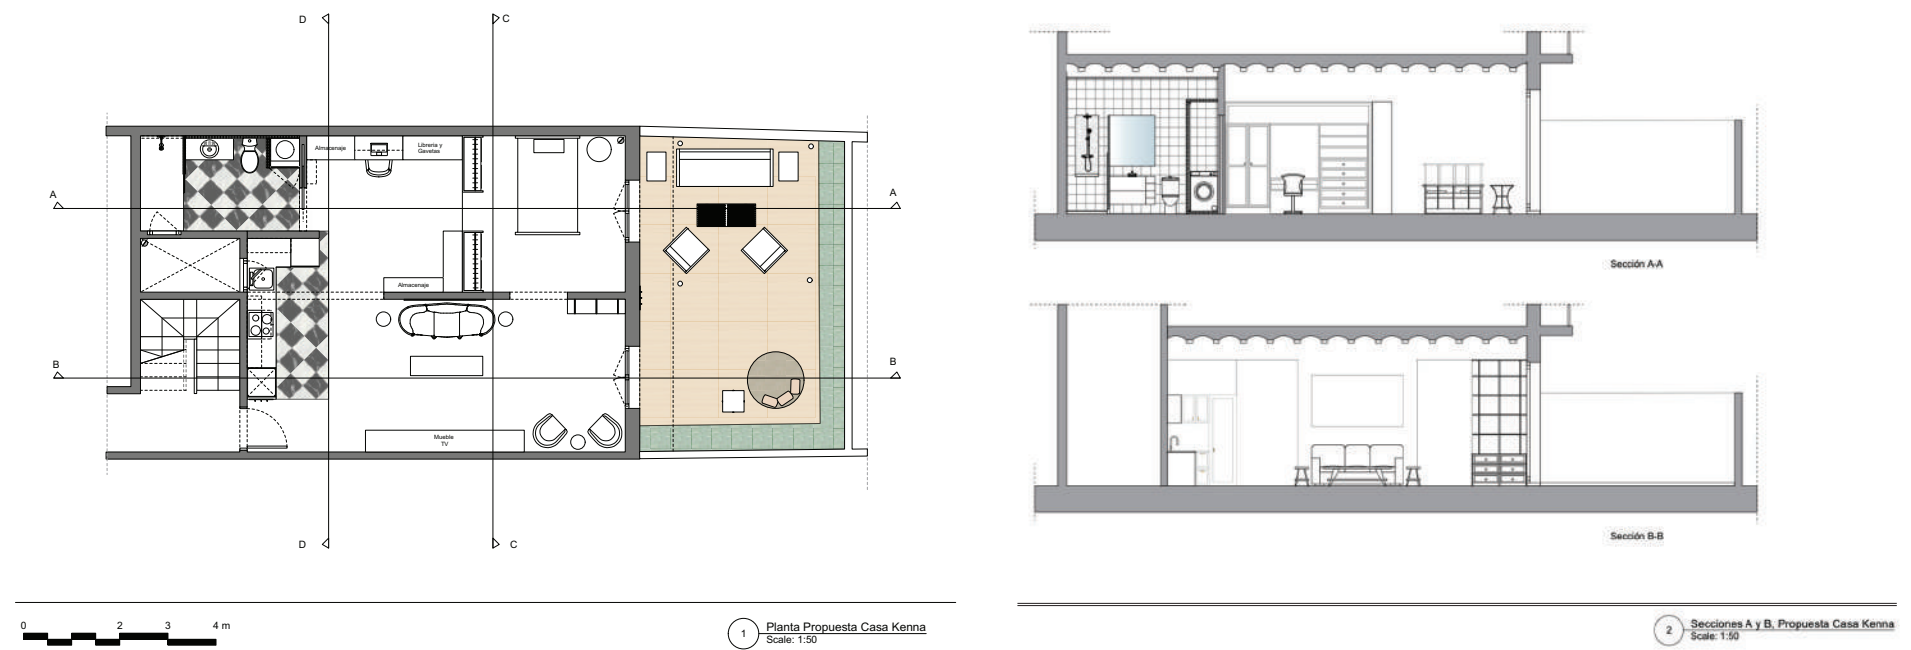

Materialidad y Mobiliario

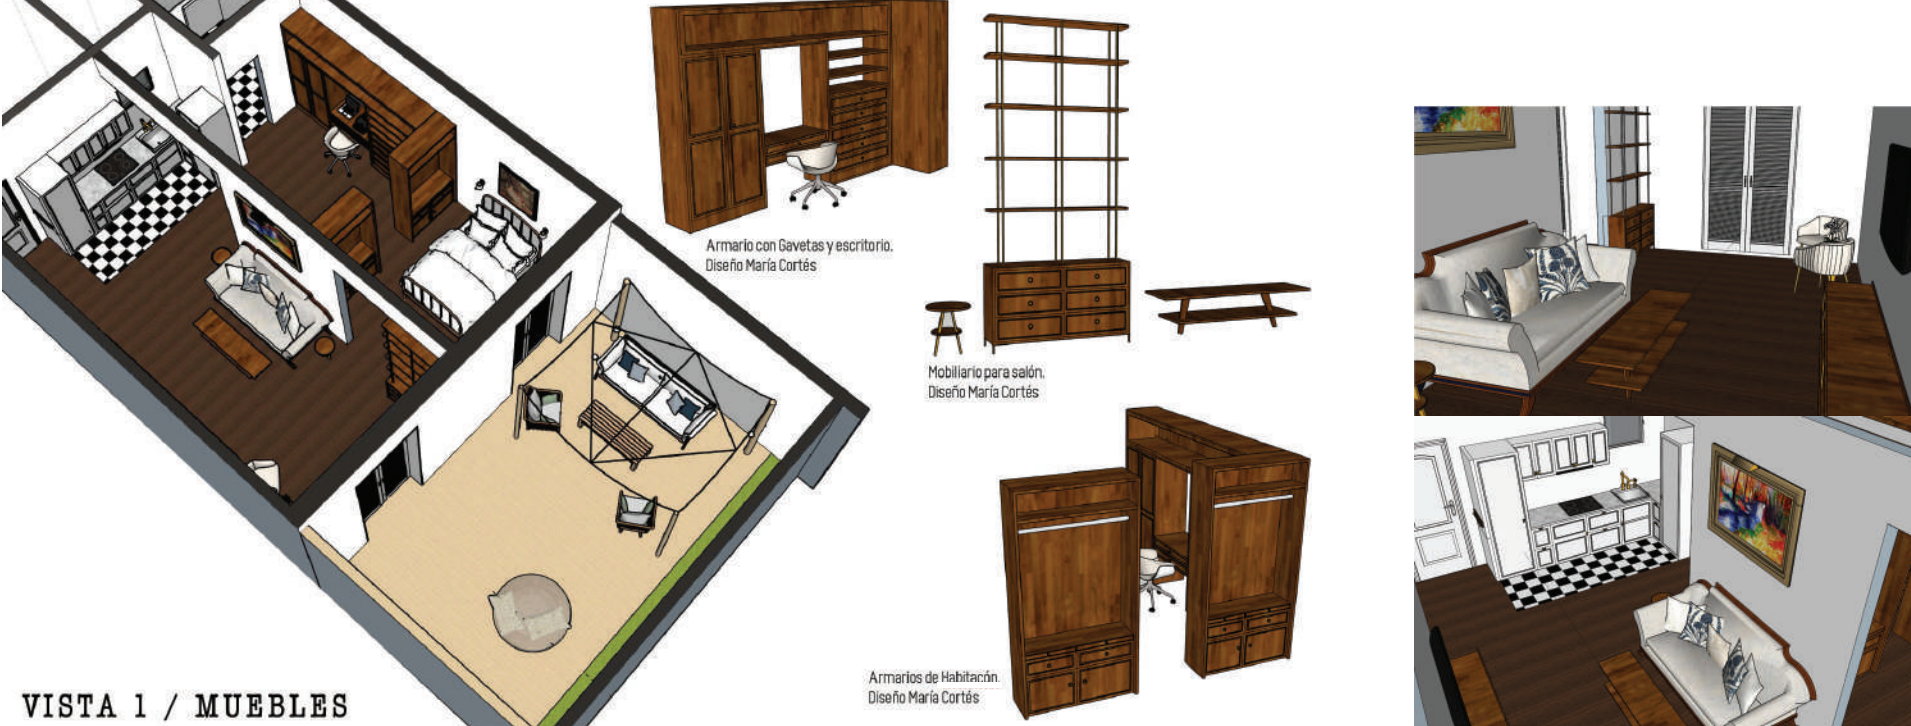

Desmond & Dempsey


Retail Design Class
2021

María Cortés, Álvaro López-Balcells, Paula Robles


Diseño Tienda Digital

Durante el curso de Diseño de Retail, como parte de un equipo de tres personas, creamos una propuesta para el diseño de la tienda física de la marca Desmond & Dempsey, conocida por su tienda digital de pijamas. Nos sumergimos en el espíritu de la marca, sus valores y la impresión que deseaba transmitir a los usuarios. Optamos por una paleta de colores y una atmósfera tropical, delicada y relajada, que reflejara la esencia de la marca. Un aspecto crucial de este proyecto fue considerar al usuario en su totalidad: su perfil, sus expectativas de una marca como esta y cómo queríamos que interactuara con la tienda. Utilizamos moodboards, recorridos virtuales y diseño de espacios para llegar a nuestro diseño final, creando una narrativa que no solo representara a la marca, sino también al usuario.


Valores

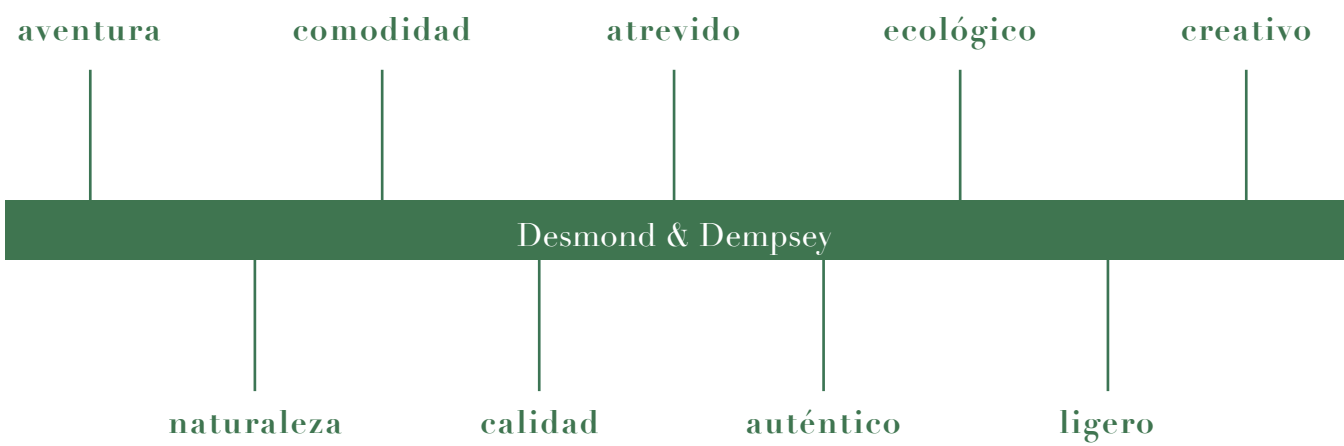


Zonificación

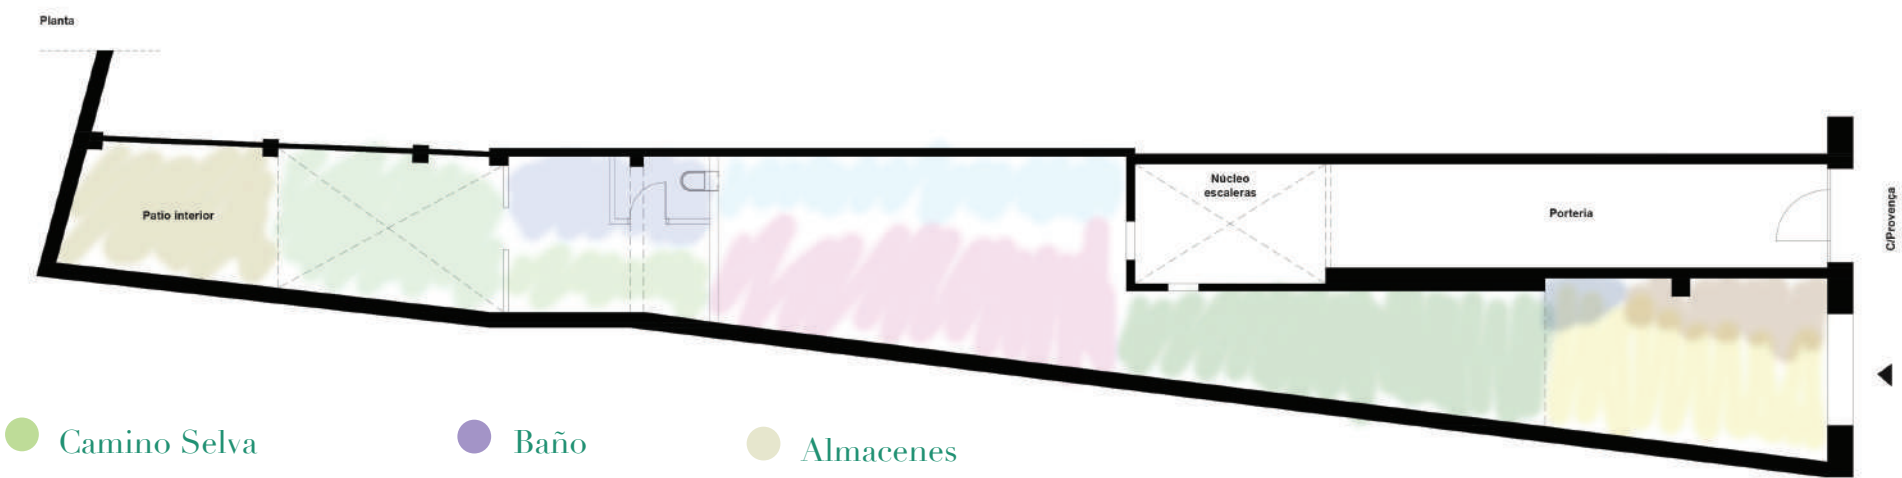


Recorridos

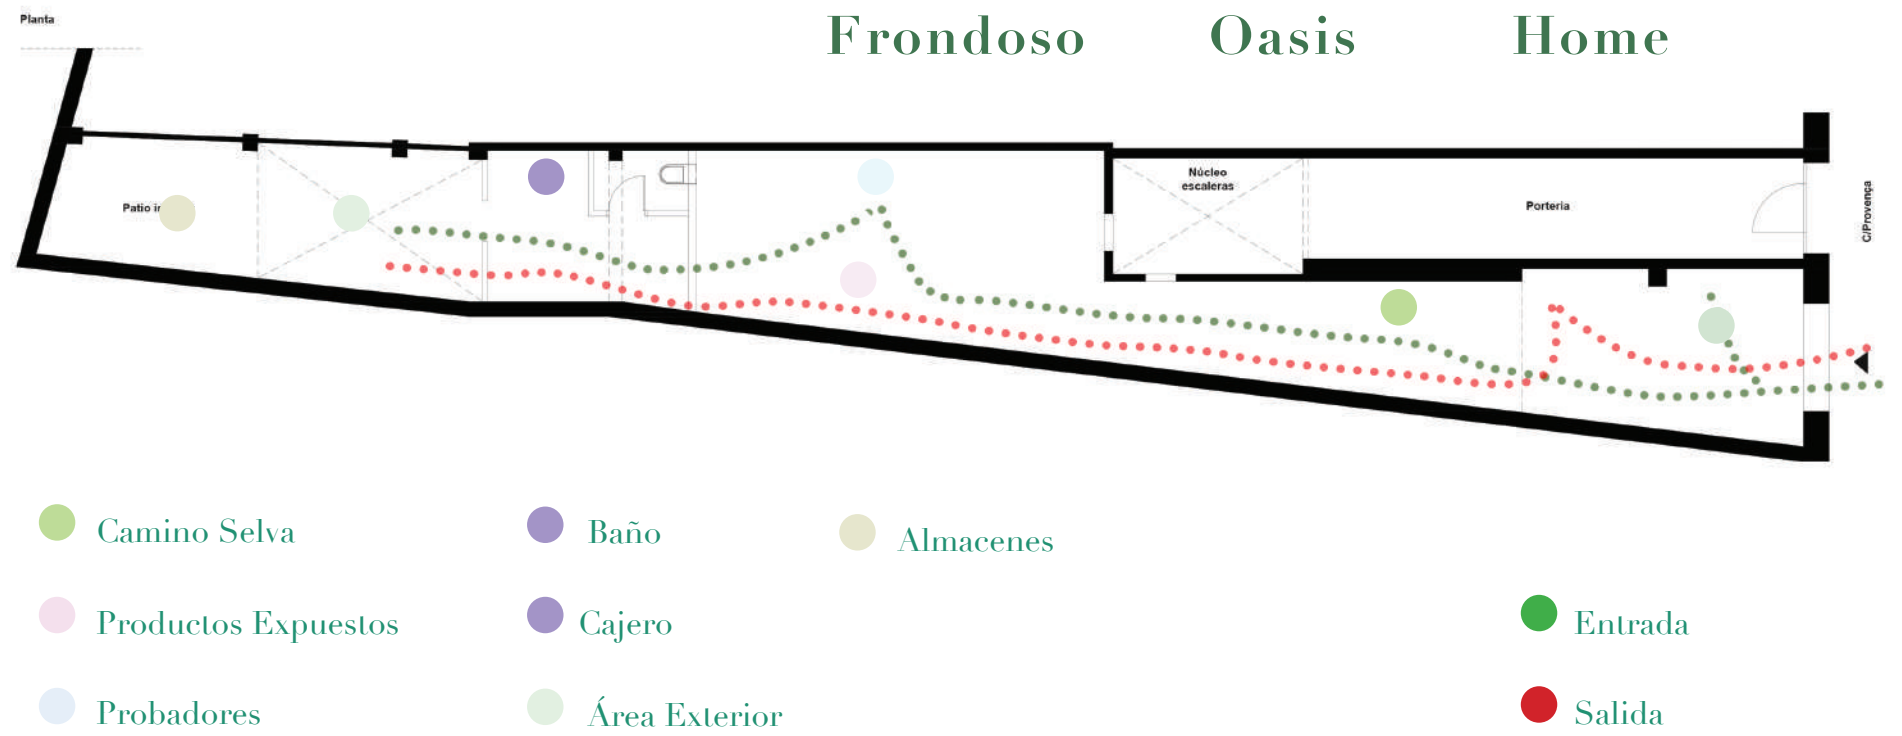


Planta y Alzados

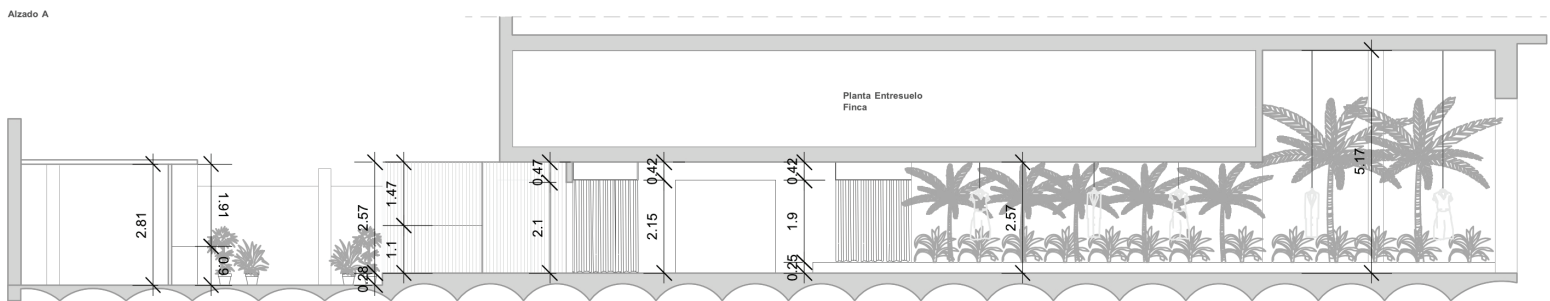

Alzado A

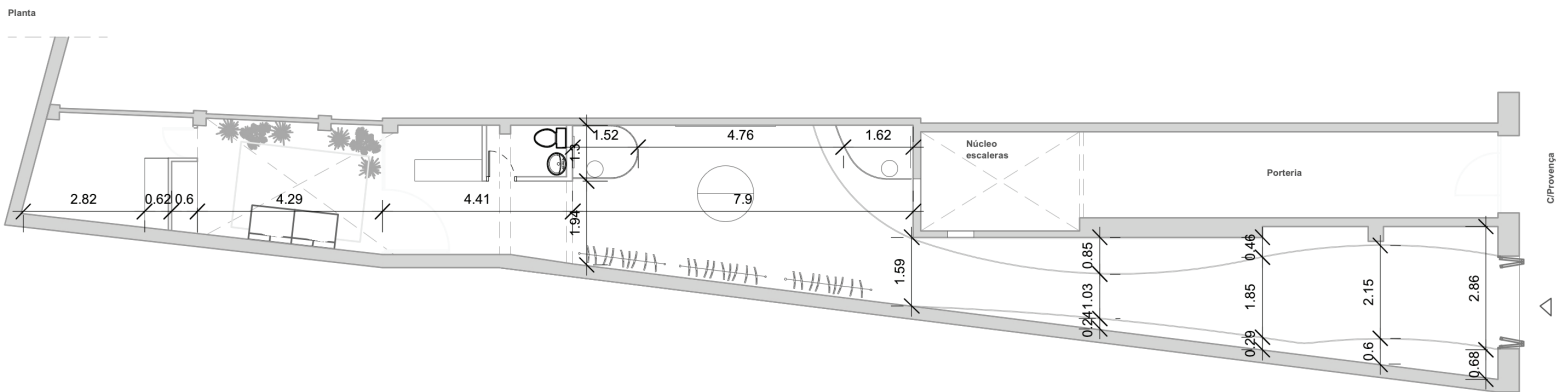


Planta

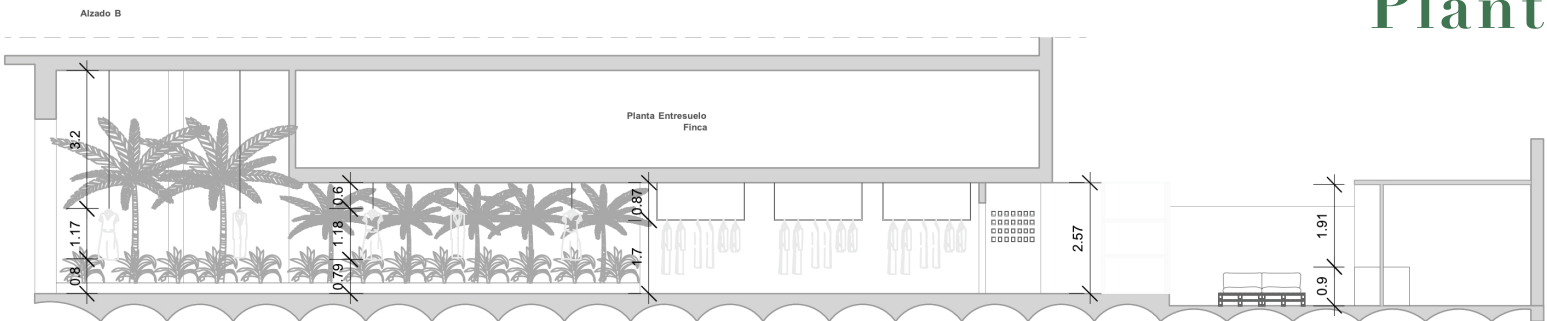

Alzado B

Iluminación

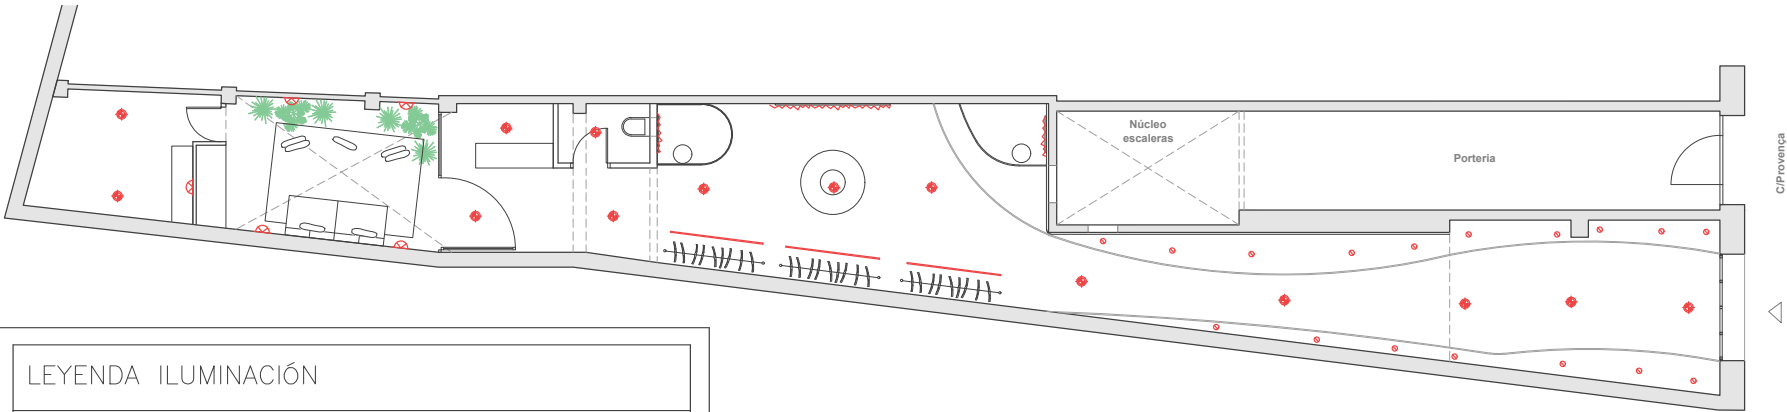

LEYENDA ILUMINACIÓN	
	Punto de luz empotrada. LED
	Aplique de pared. LED.
	Riel Wallwash
	Tira de LED
	Foco Exterior de Suelo

General



Luz empotrada Deep Ringo Trimless LED -Delta Light

Especifica




Luz de suelo. Frax M 930 Linear H - Delta Light



Luz Suspendida WallWash 12. Dot.Com on - Delta Light


Decorativa

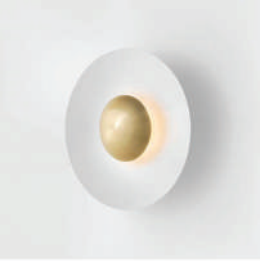


Aplique de Pared coss60, ISOS Lámpara De Pie redondo de metal - Alazáen Ratán - Wabi Home




Planta

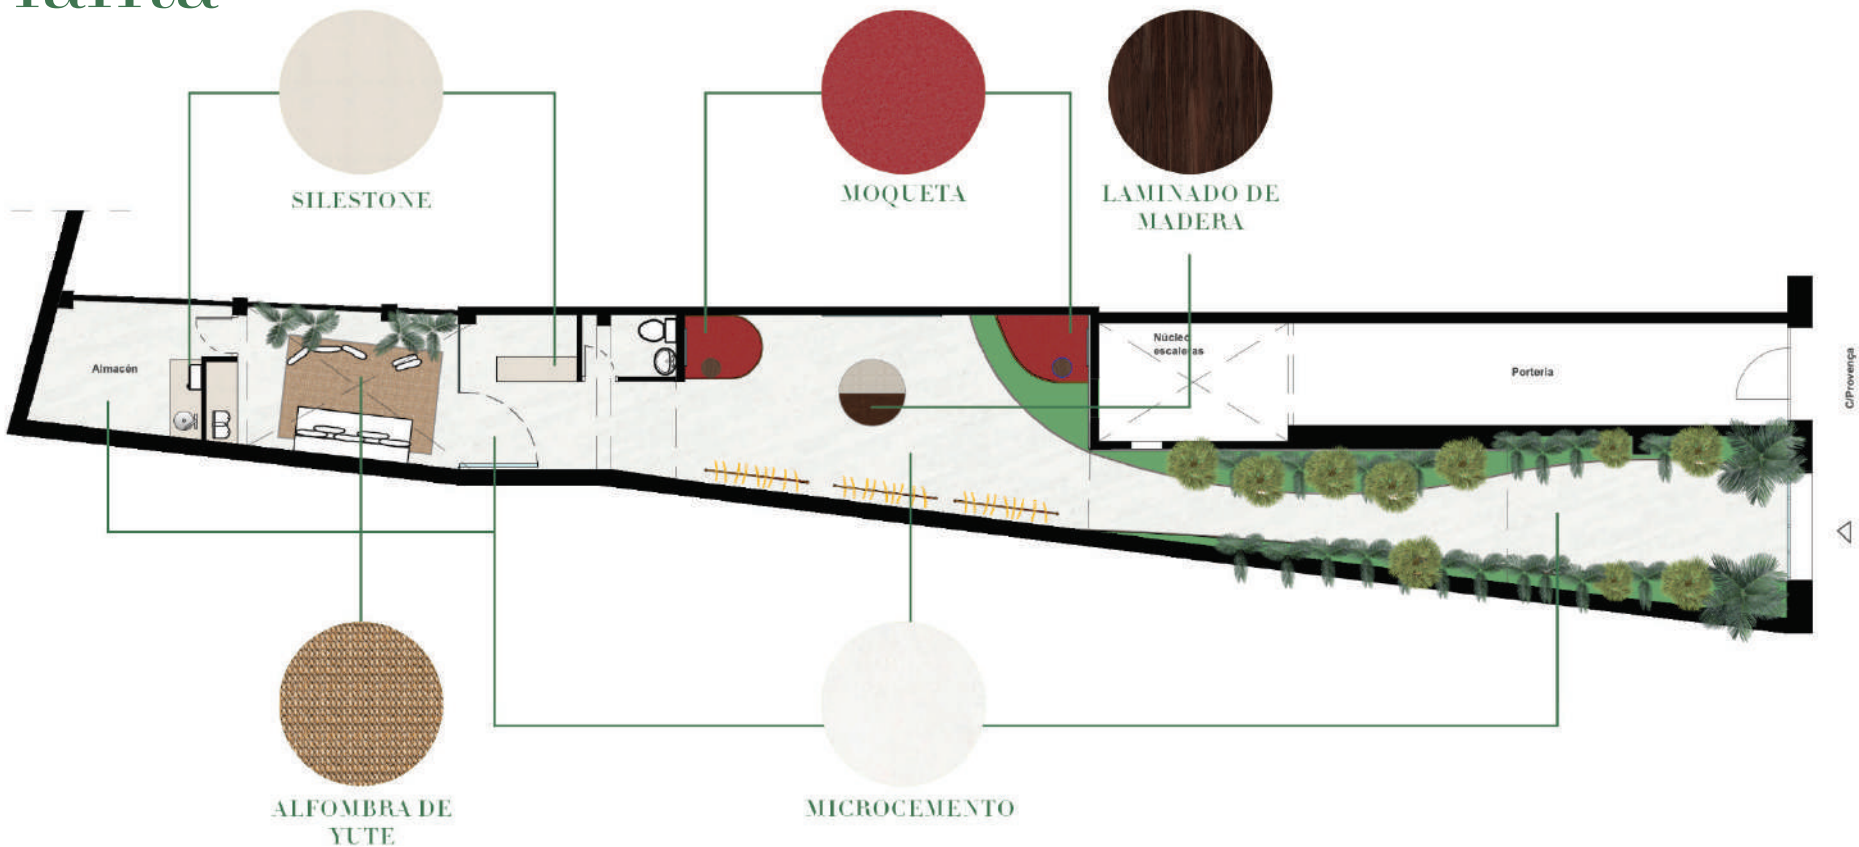

Alzado A

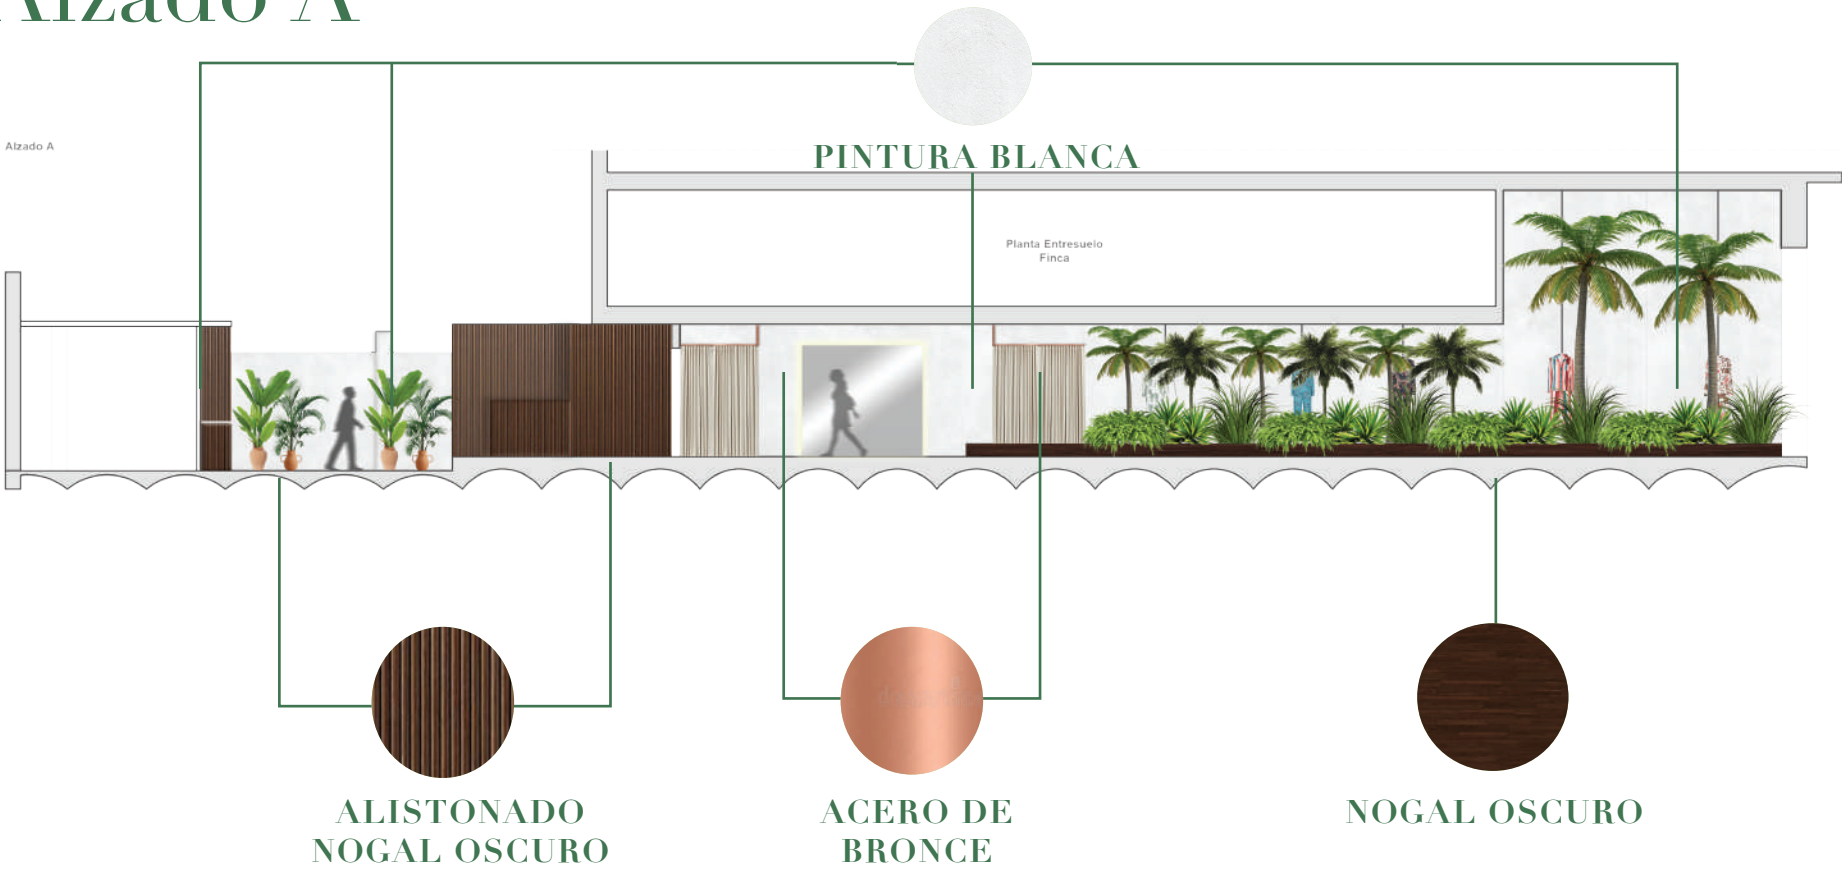


Alzado B

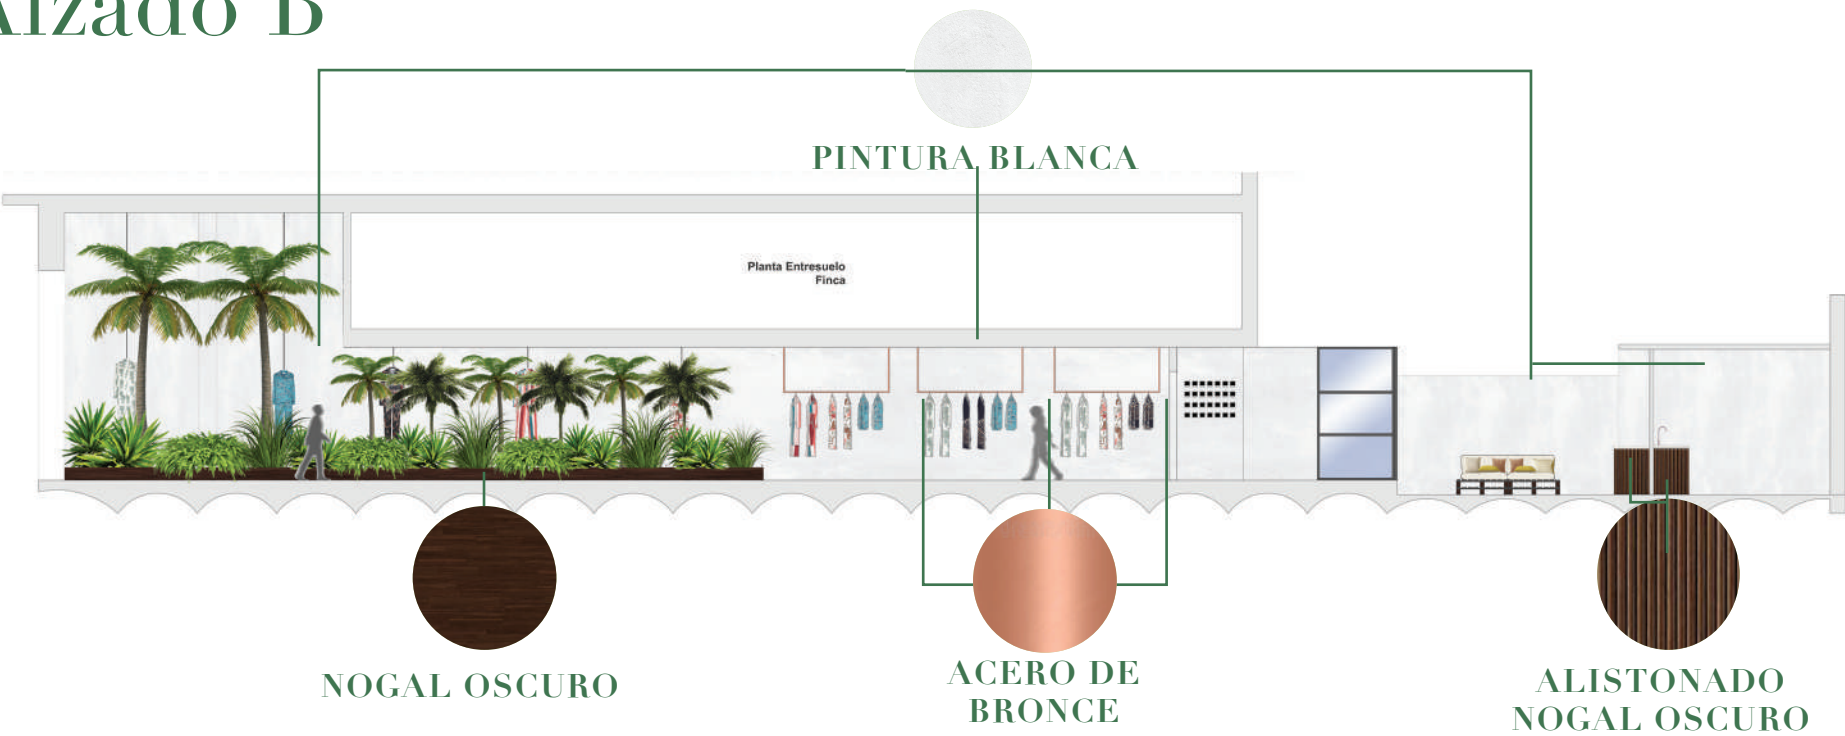

Materiales

Detalles

Entrada

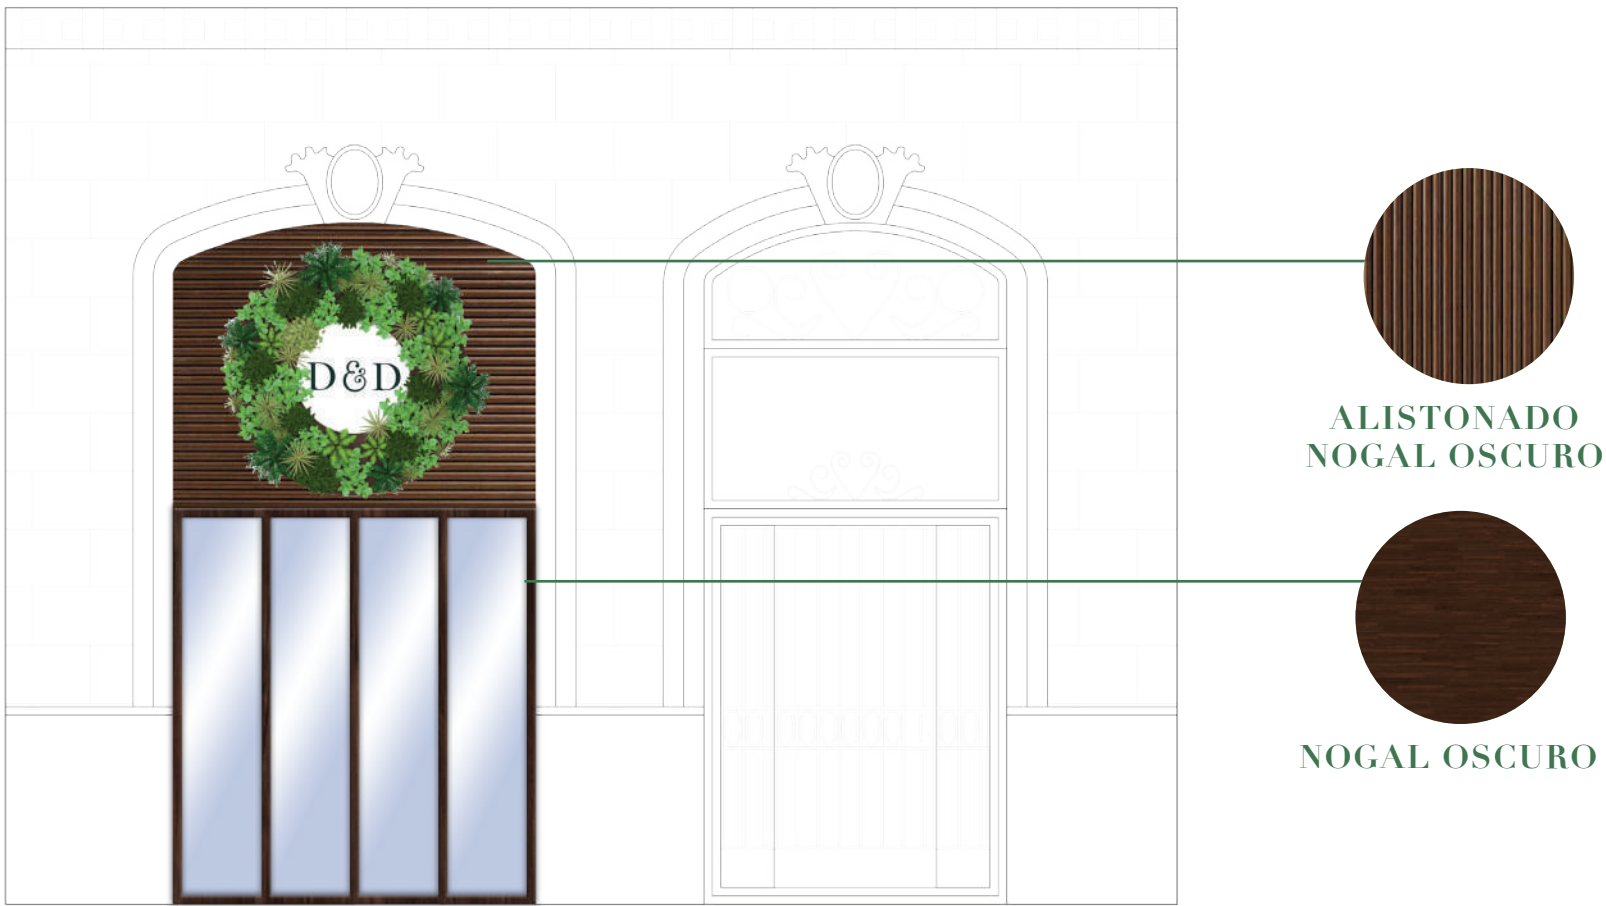

Probador



Estanteria/Asiento Central



PROYECTOS
PROFESIONALES



Residencia Unifamiliar



VIVIENDA UNIFAMILIAR


ANTISTIANA 23

Estudio Roarquitectos

En mi experiencia en el estudio Roarquitectos, tuve el privilegio de participar en el diseño de una vivienda unifamiliar en Cataluña, destinada a una pareja de jubilados. Su visión para el diseño era clara: buscaban formas simples y espacios lo más abiertos posible. En respuesta a esto, optamos por un diseño que integrara un amplio salón con cocina y comedor en un espacio de doble altura, fomentando la sensación de amplitud y luminosidad.

Uno de los aspectos destacados del proyecto fue la atención a los dormitorios. Considerando la posibilidad de visitas y familiares, se planificaron al menos tres dormitorios adicionales, además de una suite completa para la pareja, equipada con múltiples baños para garantizar la comodidad y privacidad en cada habitación.


El diseño del espacio exterior también fue cuidadosamente considerado. Se optó por formas simples pero impactantes visualmente, que contrastaban hábilmente con la paleta de colores seleccionada, creando un entorno armonioso y atractivo.

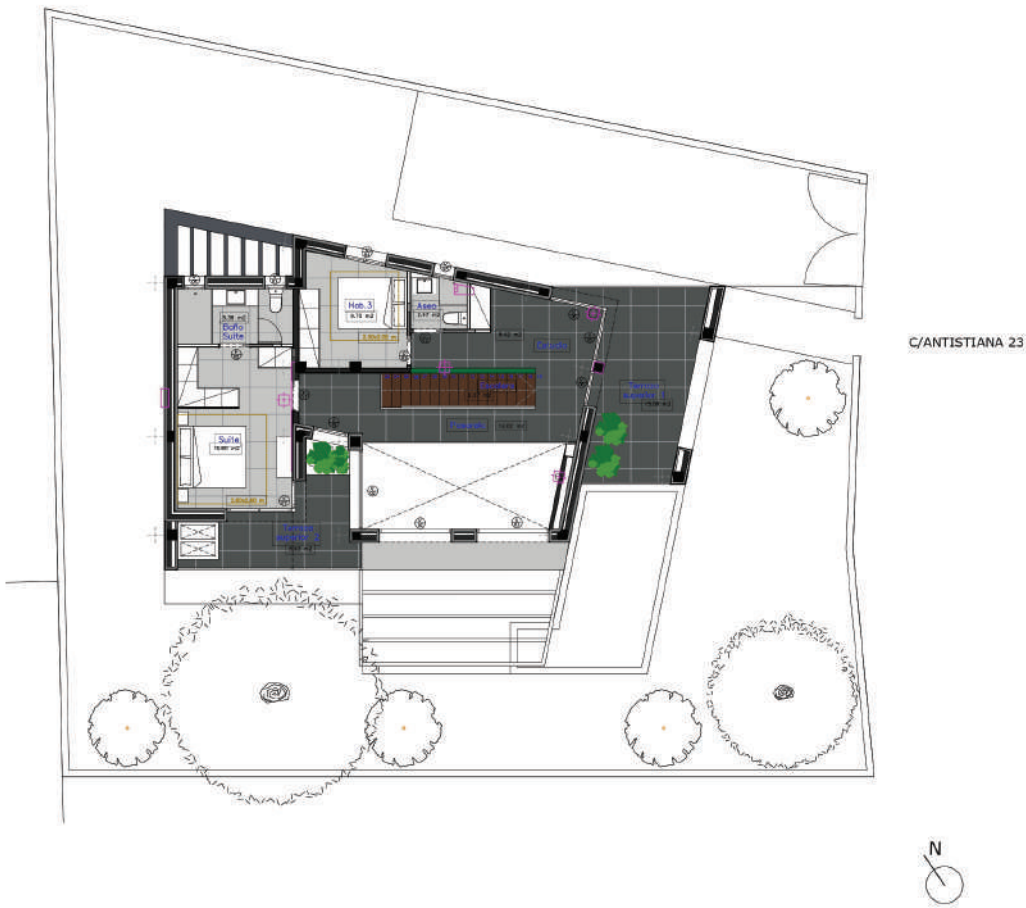


ALZADOS




ALZADO SUR

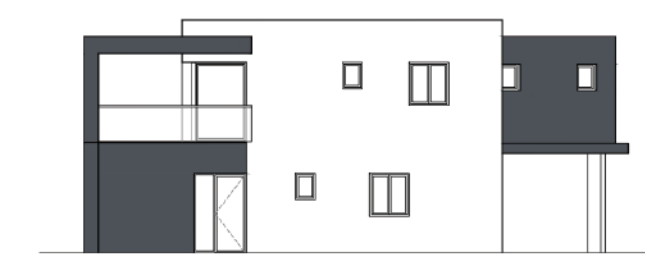

ALZADO NORTE

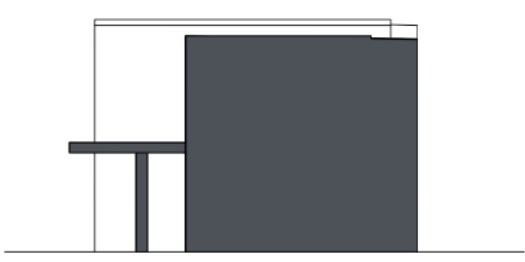


ALZADO OESTE

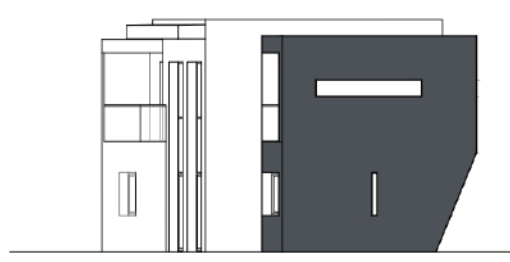


ALZADO ESTE


SECCIONES

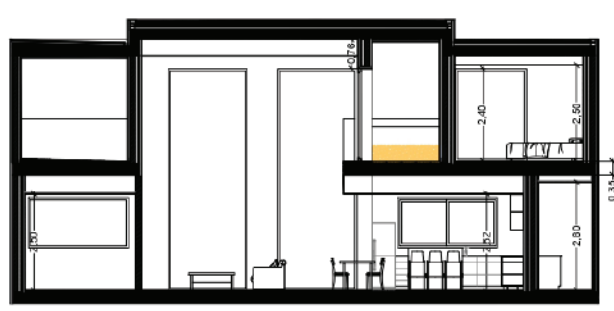

SECCIÓN A-A'

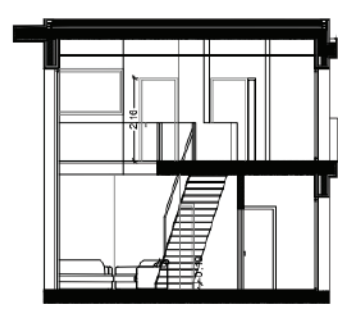

SECCIÓN B-B'

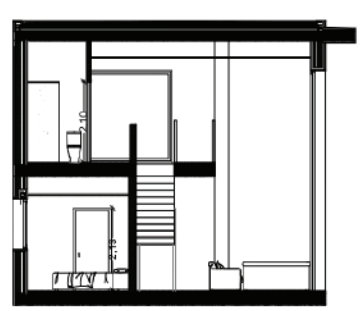

SECCIÓN C-C'

VISTAS 3D

EXTERIOR

VISTA FRONTAL



EXTERIOR



VISTAS 3D

INTERIOR

SALÓN



COCINA/COMEDOR





+34 663 58 50 81



mariacv1993@gmail.com



<https://www.linkedin.com/in/mariacortesv24/>



Barcelona, España

